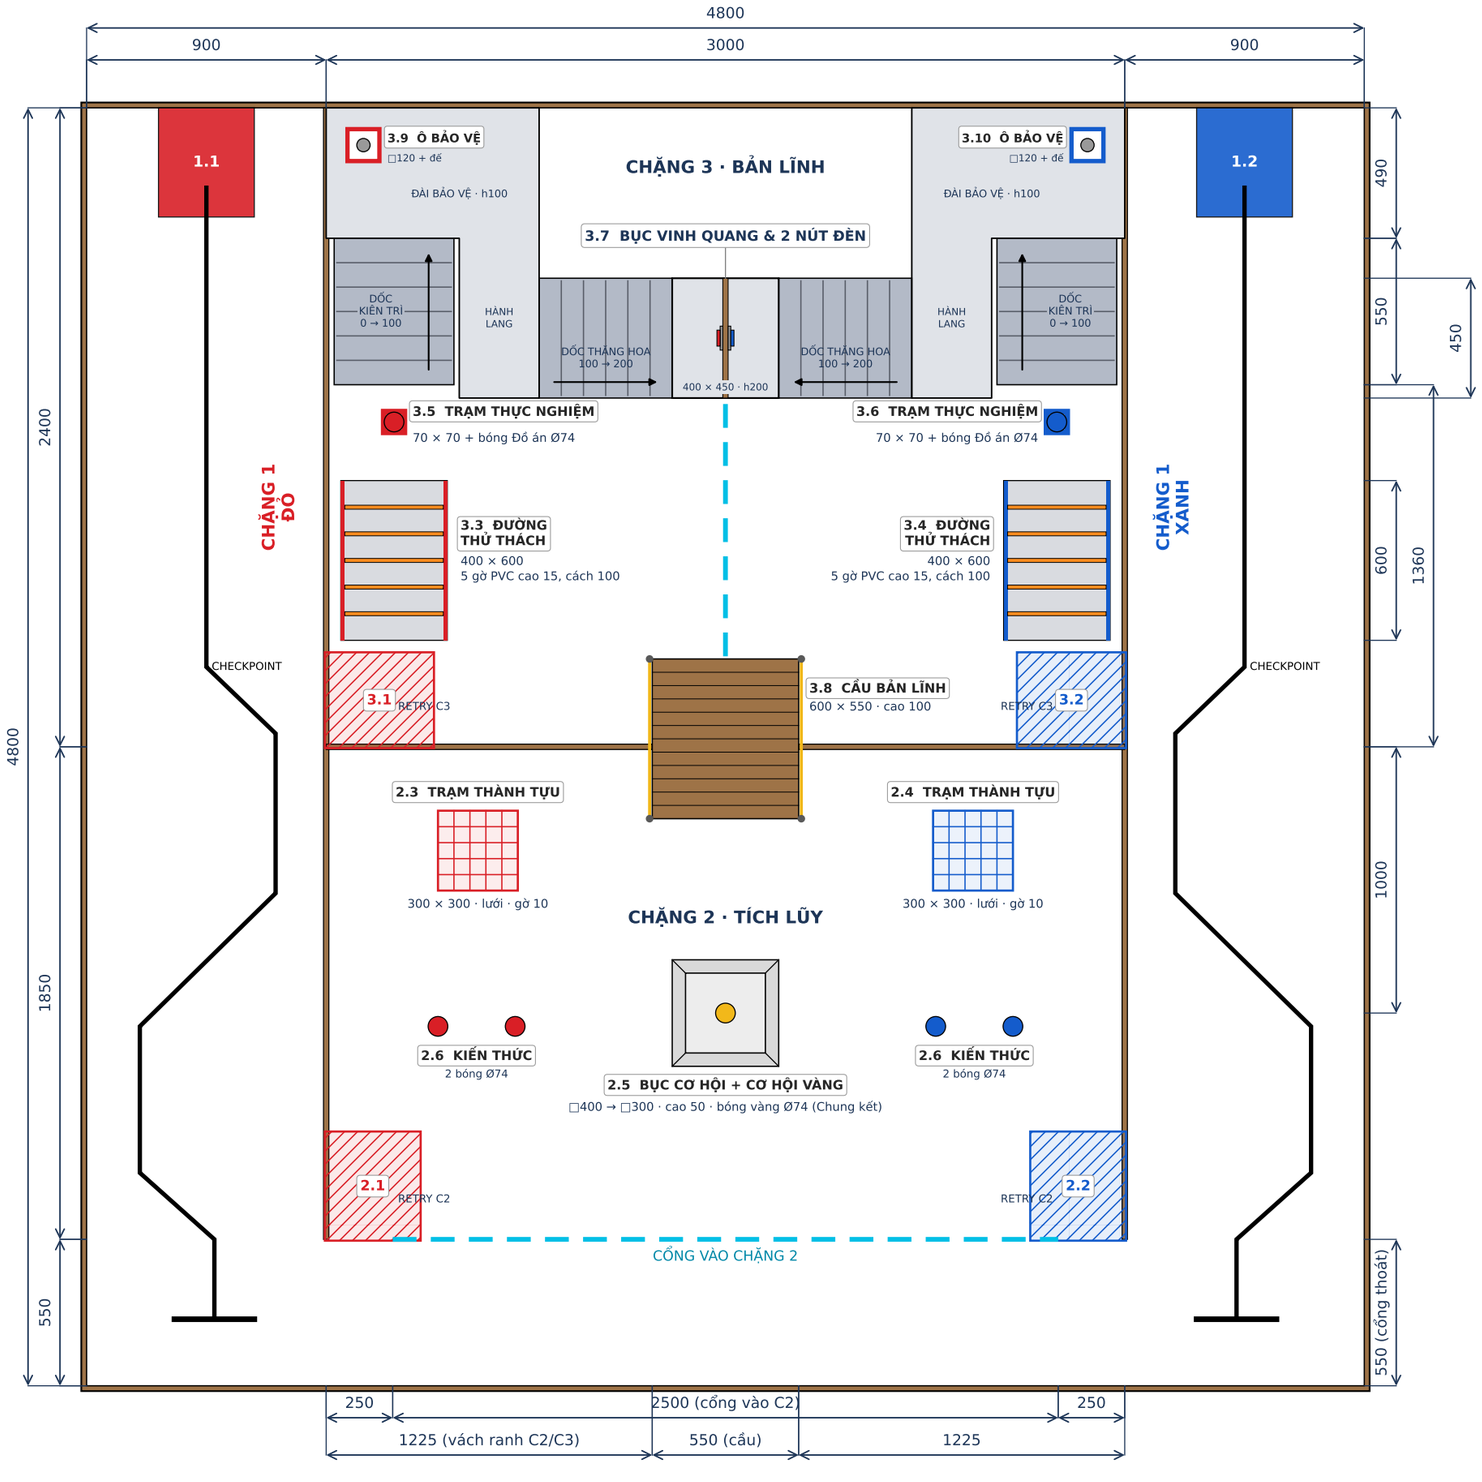



## BẢNG THÔNG SỐ SA BÀN

| | |
|---|---|
| **Kích thước tổng** | 4800 × 4800 mm, khung cao 100 mm |
| **Làn dò line (×2)** | 900 × 4800 mm, vạch đen 20 mm |
| **1.1–1.2 Trạm khởi hành** | 410 × 360 mm (đỉnh làn) |
| **Đường Danh vọng** | thẳng 1800 mm → Checkpoint (không khung) |
| **Đường Thách thức** | ziczac 45°, 2050 mm → vạch chữ T 300 mm |
| **Khu Chặng 2** | 3000 × 1850 mm |
| **2.1–2.2 Retry C2** | 410 × 360 mm, góc dưới, gạch chéo 45° |
| **2.3–2.4 Trạm thành tựu** | 300 × 300 mm, lưới, gờ chặn bóng 10 |
| **2.5 Bục Cơ hội** | □400 → □300, cao 50; bóng vàng Ø74 |
| **2.6 Kiến thức** | 4 bóng pickleball Ø74 (2 Đỏ, 2 Xanh) |
| **Khu Chặng 3** | 3000 × 2400 mm, nét đứt chia đôi |
| **3.1–3.2 Retry C3** | 410 × 360 mm, sát vách làn |
| **3.3–3.4 Đường Thử thách** | 400 × 600 mm, 5 gờ PVC cao 15, cách 100 |
| **3.5–3.6 Trạm Thực nghiệm** | 70 × 70 mm + bóng Đồ án Ø74 màu đội |
| **3.7 Dốc Kiên trì** | 550 × 450 mm, dốc 10°, cao 0 → 100 |
| **Đài Bảo vệ** | chữ L sát mép trên sân, cao 100 |
| **Dốc Thăng hoa** | 500 × 450 mm, dốc 10°, cao 100 → 200 |
| **Bục Vinh Quang** | 400 × 450 mm, cao 200, vách ngăn giữa |
| **Nút Đèn Vinh Quang** | 2 nút trên 2 mặt vách, ấn theo phương X |
| **3.8 Cầu Bản lĩnh** | 600 × 550 × 100 mm, lối duy nhất C2→C3 |
| **3.9–3.10 Ô Bảo vệ Đồ án** | □120, gờ 10, đế nhỏ đặt bóng Đồ án |

### CHÚ THÍCH

- Đội Đỏ
- Đội Xanh
- Bóng Cơ hội vàng / dây cầu
- Gờ ống PVC Đường Thử thách
- Bục Vinh Quang (dốc: xám, mũi tên = hướng lên)
- Khu Retry
- Trạm thành tựu (lưới)
- Vách / khung / Cầu Bản lĩnh (gỗ)
- Cổng vào Chặng 2 / ranh giữa Chặng 3 (nét đứt cyan)
- Đường dò line 20 mm

## SA BÀN THI ĐẤU ENGINEERING PATH 2026

Khoa Cơ khí · HCM-UTE
Theo Thể lệ chính thức ENGINEERING PATH 2026

Đơn vị: mm · Mặt bằng (hình chiếu bằng)

Tỉ lệ: 1:30 (A3)
Ngày: 31/10/2026

Tờ 1/1 · Bản chính thức