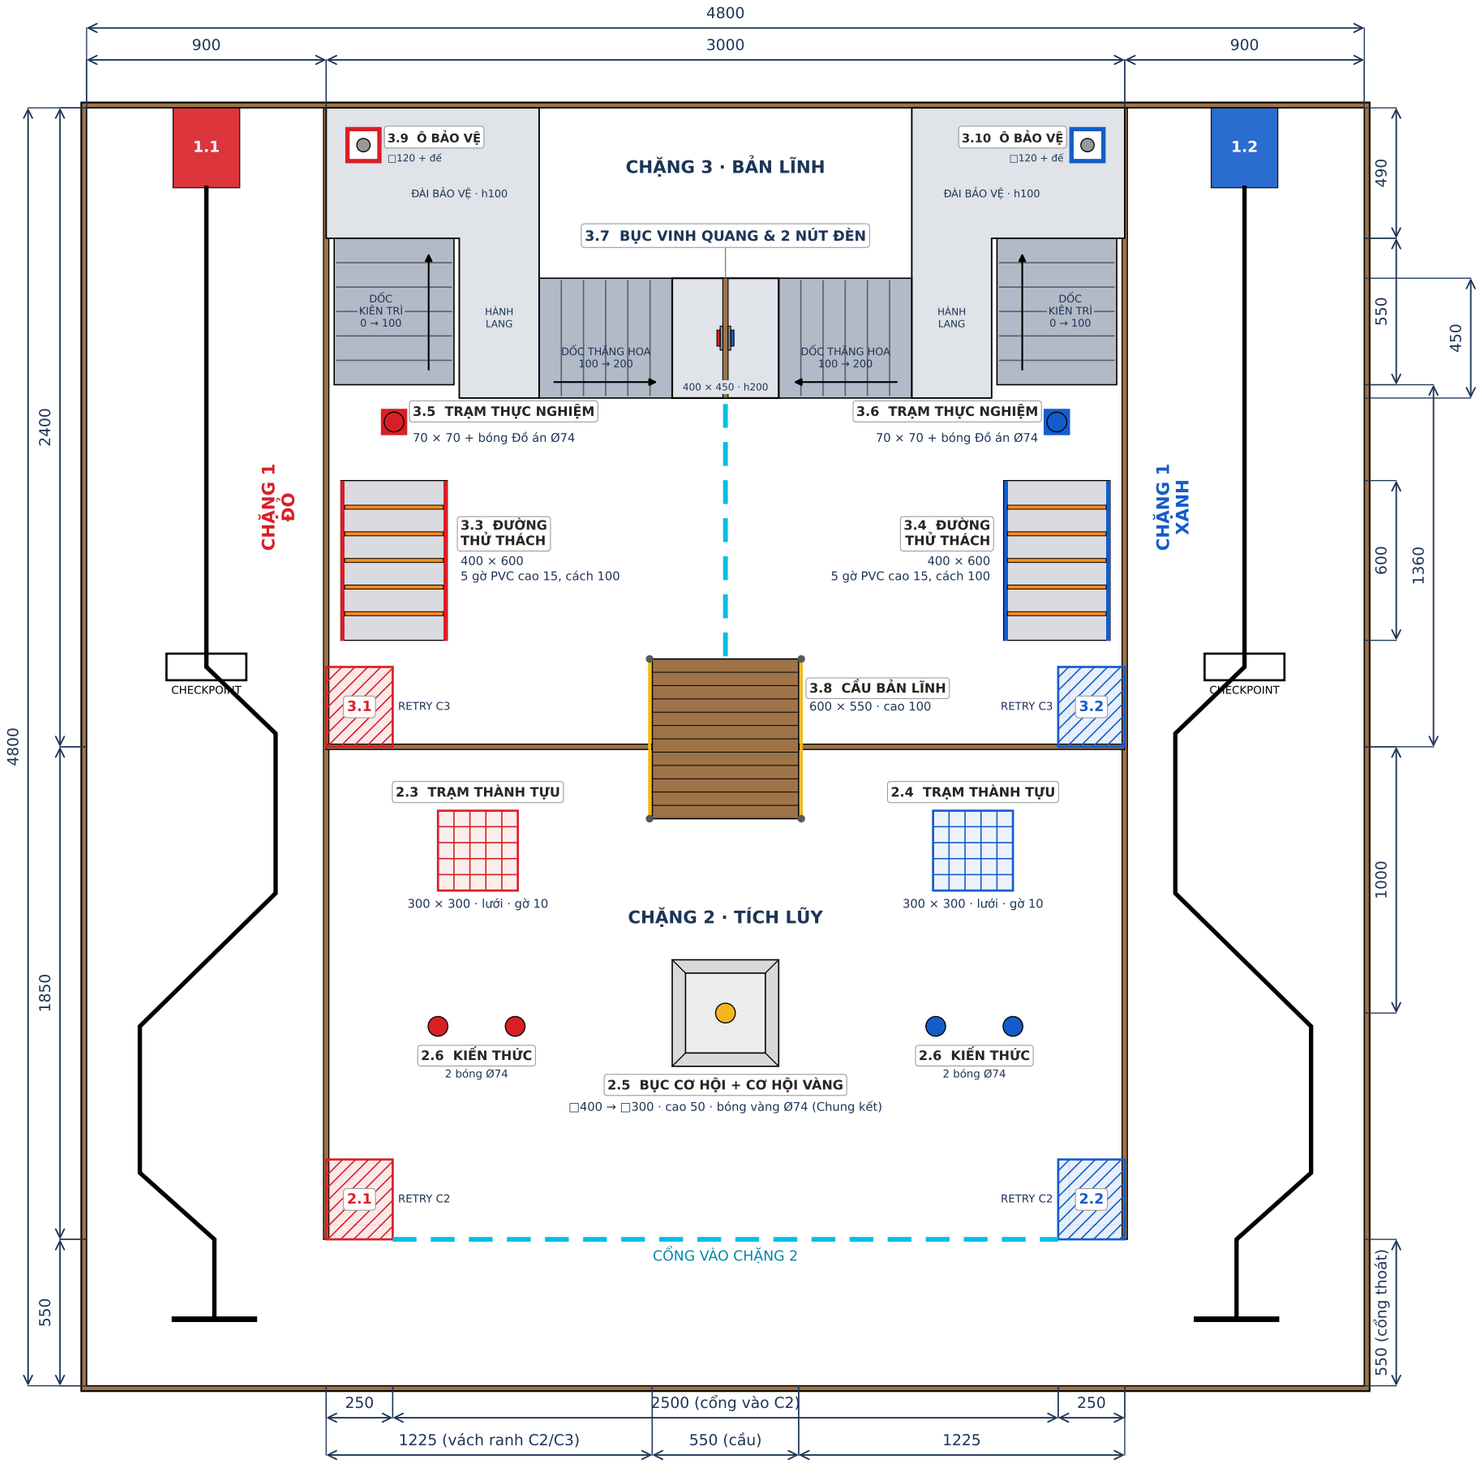


BẢNG THÔNG SỐ SA BÀN

Kích thước tổng	4800 × 4800 mm, khung cao 100 mm
Làn dò line (×2)	900 × 4800 mm, vạch đen 20 mm
1.1–1.2 Trạm khởi hành	300 × 250 mm (đỉnh làn)
Đường Danh vọng	thẳng 1800 mm → Checkpoint
Đường Thách thức	ziczac 45° → vạch chữ T 300 mm
Khu Chặng 2	3000 × 1850 mm
2.1–2.2 Retry C2	250 × 300 mm, góc dưới, gạch chéo 45°
2.3–2.4 Trạm thành tựu	300 × 300 mm, lưới, gờ chặn bóng 10
2.5 Bục Cơ hội	□400 → □300, cao 50; bóng vàng Ø74
2.6 Kiến thức	4 bóng pickleball Ø74 (2 Đỏ, 2 Xanh)
Khu Chặng 3	3000 × 2400 mm, nét đứt chia đôi
3.1–3.2 Retry C3	250 × 300 mm, sát vách làn
3.3–3.4 Đường Thử thách	400 × 600 mm, 5 gờ PVC cao 15, cách 100
3.5–3.6 Trạm Thực nghiệm	70 × 70 mm + bóng Đồ án Ø74 màu đội
3.7 Dốc Kiên trì	550 × 450 mm, dốc 10°, cao 0 → 100
Đài Bảo vệ	chữ L sát mép trên sân, cao 100
Dốc Thăng hoa	500 × 450 mm, dốc 10°, cao 100 → 200
Bục Vinh Quang	400 × 450 mm, cao 200, vách ngăn giữa
Nút Đèn Vinh Quang	2 nút trên 2 mặt vách, ấn theo phương X
3.8 Cầu Bản lĩnh	600 × 550 × 100 mm, lối duy nhất C2→C3
3.9–3.10 Ô Bảo vệ Đồ án	□120, gờ 10, đế nhỏ đặt bóng Đồ án

CHÚ THÍCH

- Đội Đỏ
- Đội Xanh
- Bóng Cơ hội vàng / dây cầu
- Gờ ống PVC Đường Thử thách
- Bục Vinh Quang (dốc: xám, mũi tên = hướng lên)
- Khu Retry
- Trạm thành tựu (lưới)
- Vách / khung / Cầu Bản lĩnh (gỗ)
- Cổng vào Chặng 2 / ranh giữa Chặng 3 (nét đứt cyan)
- Đường dò line 20 mm

SA BÀN THI ĐẤU ENGINEERING PATH 2026

Khoa Cơ khí · HCM-UTE
Theo Thể lệ (3) ENGINEERING PATH 2026

Đơn vị: mm · Mặt bằng (hình chiếu bằng)

Tỉ lệ: 1:30 (A3)
Ngày: 29/10/2026

Tờ 1/1 · Bản dự thảo