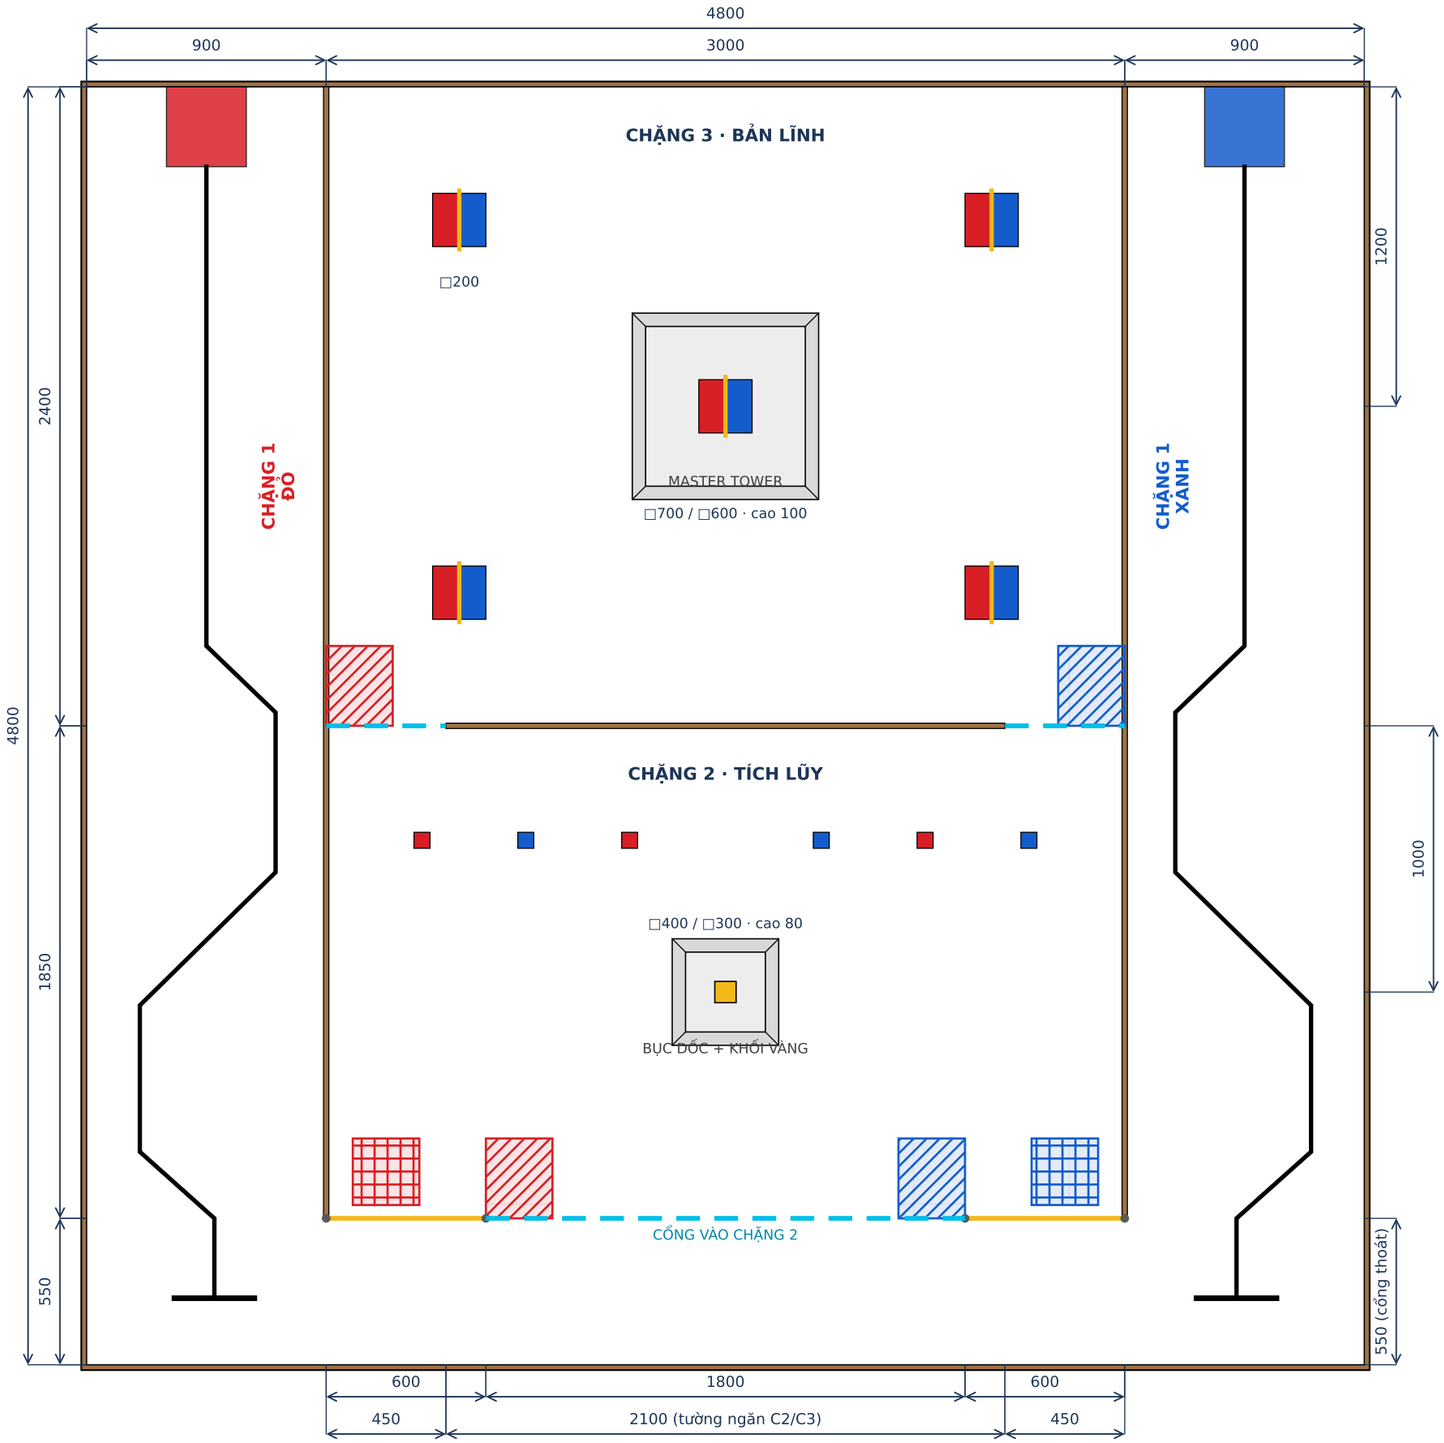


BẢNG THÔNG SỐ SA BÀN

Kích thước tổng	4800 × 4800 mm, khung cao 100 mm
Làn dò line (×2)	900 × 4800 mm, vạch đen 25 mm
Ô xuất phát	300 × 300 mm (đỉnh làn)
Vạch chữ T	300 mm · cổng thoát 550 mm
Khu Chặng 2	3000 × 1850 mm
Ô tập kết (×2)	250 × 250 mm, họa tiết lưới
Ô Retry C2 (×2)	250 × 300 mm, gạch chéo 45°
Khối cấu kiện	6 × □60 mm (3 Đỏ, 3 Xanh)
Bục dốc C2	□400 → □300, cao 80 mm
Khối Vàng	□80 mm trên đỉnh bục
Khu Chặng 3	3000 × 2400 mm
Cửa thông (×2)	450 mm nét đứt cyan
Tường ngăn	2100 mm, kiên cố
Ô Retry C3 (×2)	250 × 300 mm, sát vách biên
Cứ điểm góc (×4)	□200 mm, trục lật vàng
Master Tower	□700 → □600, cao 100 mm
Master Point	□200 mm trên đỉnh tháp

CHÚ THÍCH

- Đội Đỏ
- Đội Xanh
- Khối Vàng / trục lật / dây giăng
- Ô Retry
- Ô tập kết
- Vách / khung gỗ
- Cổng / cửa thông (nét đứt cyan)
- Đường dò line 25 mm

SA BÀN THI ĐẤU ENGINEEROBOTS 2026

Khoa Cơ khí · HCM-UTE
Theo thể lệ 26/TB-BTC-ENGINEEROBOTS

Tỉ lệ: 1:30 (A3)
Ngày: 24/10/2026

Đơn vị: mm · Mặt bằng (hình chiếu bằng)

Tờ 1/1 · Bản dự thảo