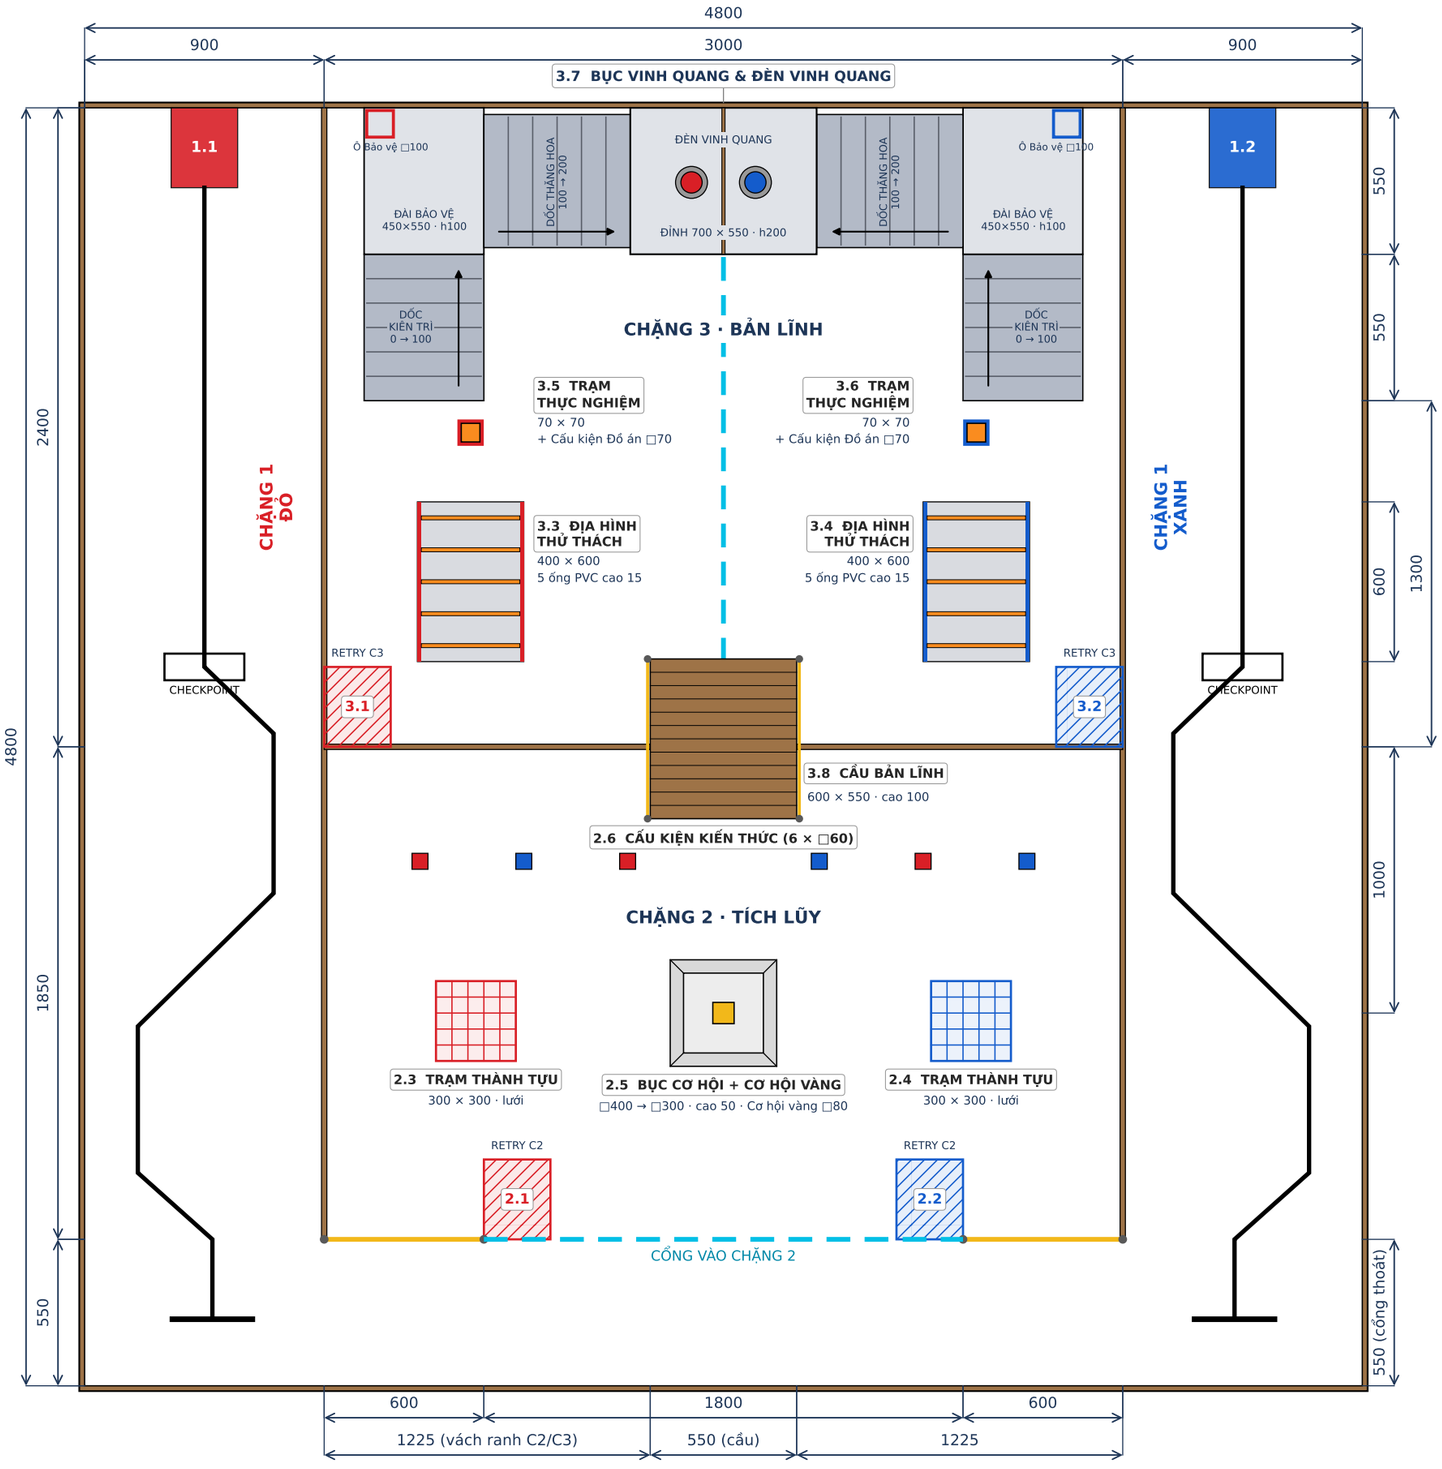


BẢNG THÔNG SỐ SA BÀN

Kích thước tổng	4800 × 4800 mm, khung cao 100 mm
Làn dò line (×2)	900 × 4800 mm, vạch đen 20 mm
1.1–1.2 Trạm khởi hành	300 × 250 mm (đỉnh làn)
Đường Danh vọng	thẳng 1800 mm → Checkpoint
Đường Thách thức	ziczac 45° → vạch chữ T 300 mm
Khu Chặng 2	3000 × 1850 mm
2.1–2.2 Retry C2	300 × 250 mm, gạch chéo 45°
2.3–2.4 Trạm thành tựu	300 × 300 mm, họa tiết lưới
2.5 Bục Cơ hội	□400 → □300, cao 50; Cơ hội vàng □80
2.6 Kiến thức	6 khối □60 mm (3 Đỏ, 3 Xanh)
Khu Chặng 3	3000 × 2400 mm, nét đứt chia đôi
3.1–3.2 Retry C3	300 × 250 mm, sát vách làn
3.3–3.4 Địa hình	400 × 600 mm, 5 ống PVC ngang cao 15
3.5–3.6 Trạm Thực nghiệm	70 × 70 mm + Cấu kiện Đồ án □70
3.7 Dốc Kiên trì	450 × 550 mm, dốc 10°, cao 0 → 100
Đài Bảo vệ	450 × 550 mm, cao 100; Ô Bảo vệ □100
Dốc Thăng hoa	550 × 500 mm, dốc 10°, cao 100 → 200
Đỉnh Bục Vinh Quang	700 × 550 mm (350 × 550/đội), cao 200
Đèn Vinh Quang	2 nút Ø80 (Đỏ / Xanh) trên đỉnh
3.8 Cầu Bản lĩnh	600 × 550 × 100 mm, lối duy nhất C2→C3

CHÚ THÍCH

- Đội Đỏ
- Đội Xanh
- Cơ hội vàng / dây giăng / dây cầu
- Cấu kiện Đồ án / ống PVC Địa hình
- Bục Vinh Quang (dốc: xám, mũi tên = hướng lên)
- Khu Retry
- Trạm thành tựu (lưới)
- Vách / khung / Cầu Bản lĩnh (gỗ)
- Cổng vào Chặng 2 / ranh giữa Chặng 3 (nét đứt cyan)
- Đường dò line 20 mm

SA BÀN THI ĐẤU ENGINEEROBOTS 2026

Khoa Cơ khí · HCM-UTE
Theo Thể lệ (2) ENGINEEROBOTS 2026

Đơn vị: mm · Mặt bằng (hình chiếu bằng)

Tỉ lệ: 1:30 (A3)
Ngày: 26/10/2026

Tờ 1/1 · Bản dự thảo