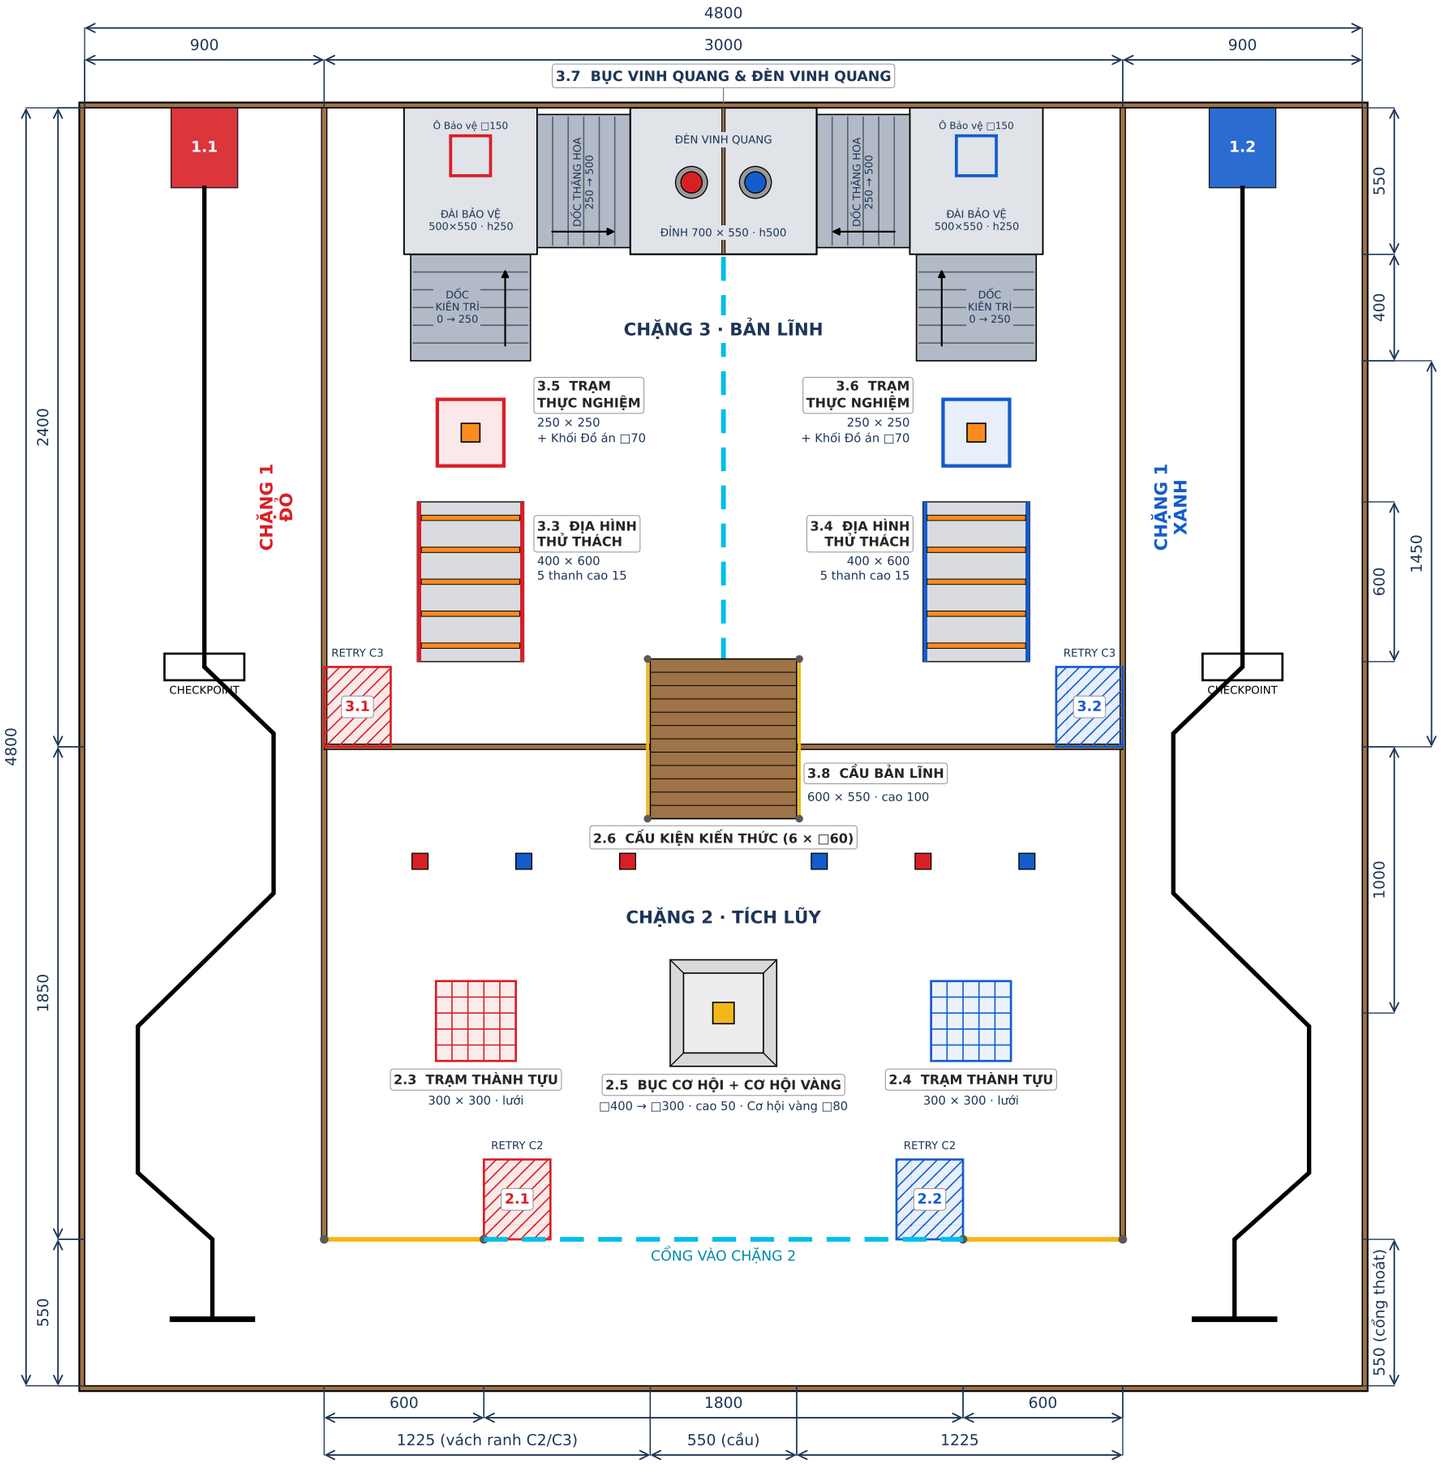


BẢNG THÔNG SỐ SA BÀN

Kích thước tổng	4800 × 4800 mm, khung cao 100 mm
Làn dò line (×2)	900 × 4800 mm, vạch đen 20 mm
1.1–1.2 Khu xuất phát	300 × 250 mm (đỉnh làn)
Đường Danh vọng	thẳng 1800 mm → Checkpoint
Đường Thách thức	ziczac 45° → vạch chữ T 300 mm
Khu Chặng 2	3000 × 1850 mm
2.1–2.2 Retry C2	300 × 250 mm, gạch chéo 45°
2.3–2.4 Trạm thành tựu	300 × 300 mm, họa tiết lưới
2.5 Bục Cơ hội	□400 → □300, cao 50; Cơ hội vàng □80
2.6 Kiến thức	6 khối □60 mm (3 Đỏ, 3 Xanh)
Khu Chặng 3	3000 × 2400 mm, nét đứt chia đôi
3.1–3.2 Retry C3	300 × 250 mm, sát vách làn
3.3–3.4 Địa hình	400 × 600 mm, 5 thanh ngang cao 15
3.5–3.6 Trạm Thực nghiệm	250 × 250 mm + Khối Đồ án □70
3.7 Dốc Kiên trì	450 × 400 mm, cao 0 → 250
Đài Bảo vệ	500 × 550 mm, cao 250; Ô Bảo vệ □150
Dốc Thăng hoa	350 × 500 mm, cao 250 → 500
Đỉnh Bục Vinh Quang	700 × 550 mm, cao 500, vách chia đôi
Đèn Vinh Quang	2 nút Ø80 (Đỏ / Xanh) trên đỉnh
3.8 Cầu Bản lĩnh	600 × 550 × 100 mm, lối duy nhất C2→C3

CHÚ THÍCH

- Đội Đỏ
- Đội Xanh
- Cơ hội vàng / dây giăng / dây cầu
- Khối Đồ án / thanh Địa hình
- Bục Vinh Quang (dốc: xám, mũi tên = hướng lên)
- Khu Retry
- Trạm thành tựu (lưới)
- Vách / khung / Cầu Bản lĩnh (gỗ)
- Cổng vào Chặng 2 / ranh giữa Chặng 3 (nét đứt cyan)
- Đường dò line 20 mm

SA BÀN THI ĐẤU ENGINEERING PATH 2026

Khoa Cơ khí · HCM-UTE
Theo thể lệ ENGINEERING PATH 2026

Đơn vị: mm · Mặt bằng (hình chiếu bằng)

Tỉ lệ: 1:30 (A3)
Ngày: 26/10/2026

Tờ 1/1 · Bản dự thảo