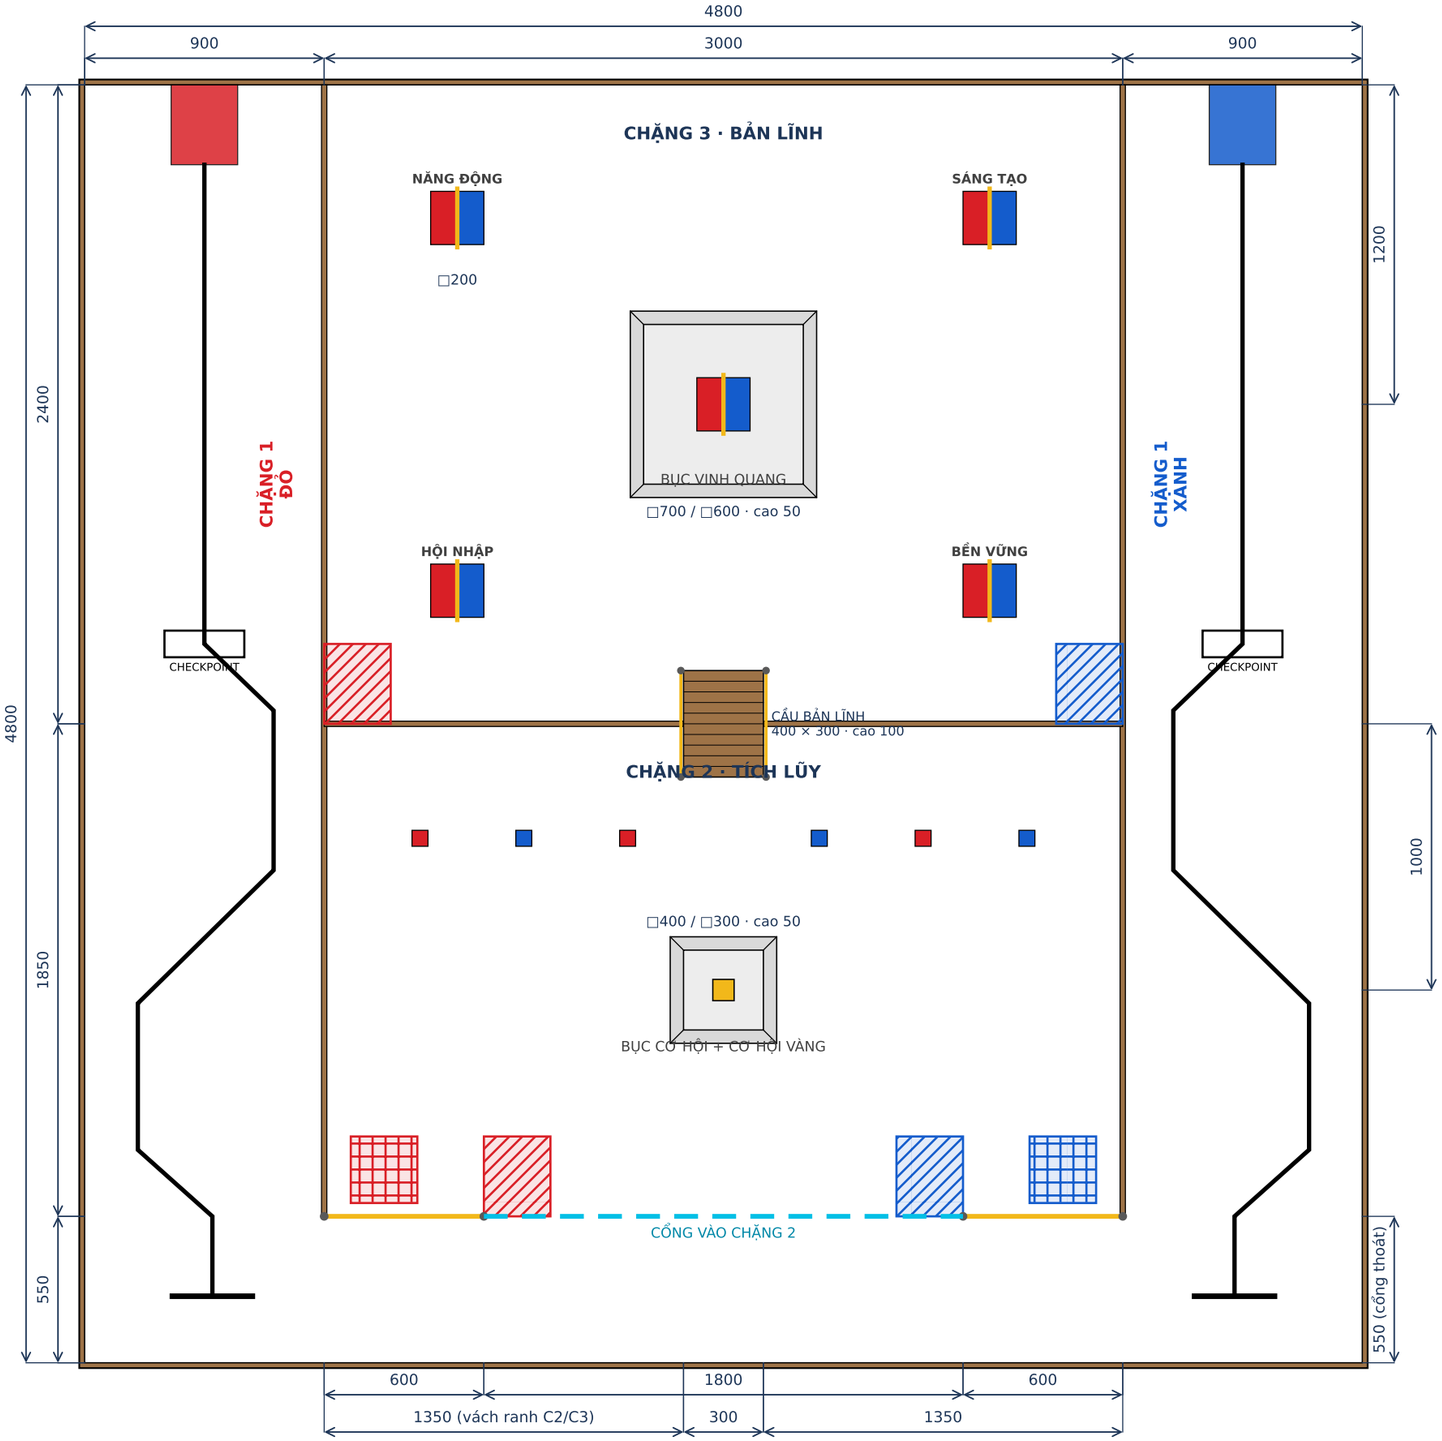


BẢNG THÔNG SỐ SA BÀN

Kích thước tổng	4800 × 4800 mm, khung cao 100 mm
Làn dò line (×2)	900 × 4800 mm, vạch đen 20 mm
Khu xuất phát	300 × 250 mm (đỉnh làn)
Đường Danh vọng	thẳng 1800 mm → Checkpoint
Đường Thách thức	ziczac 45° → vạch chữ T 300 mm
Khu Chặng 2	3000 × 1850 mm
Trạm thành tựu (×2)	250 × 250 mm, họa tiết lưới
Khu Retry C2 (×2)	300 × 250 mm, gạch chéo 45°
Cấu kiện Kiến thức	6 × □60 mm (3 Đỏ, 3 Xanh)
Bục Cơ hội	□400 → □300, cao 50 mm
Cơ hội vàng	□80 mm trên đỉnh bục
Khu Chặng 3	3000 × 2400 mm
Cầu Bản lĩnh	400 × 300 × 100 mm, dây treo
Ranh C2/C3	vách kín, lối qua duy nhất là cầu
Khu Retry C3 (×2)	300 × 250 mm, sát vách biên
Cứ điểm góc (×4)	□200 mm, trục lật vàng
Bục Vinh quang	□700 → □600, cao 50 mm
Cứ điểm Vinh quang	□200 mm trên đỉnh bục

CHÚ THÍCH

- Đội Đỏ
- Đội Xanh
- Cơ hội vàng / trục lật / dây giăng
- Khu Retry
- Trạm thành tựu
- Vách / khung gỗ
- Cổng vào Chặng 2 (nét đứt cyan)
- Đường dò line 20 mm

SA BÀN THI ĐẤU ENGINEEROBOTS 2026

Khoa Cơ khí · HCM-UTE
Theo thể lệ 26/TB-BTC-ENGINEEROBOTS

Tỉ lệ: 1:30 (A3)
Ngày: 24/10/2026

Đơn vị: mm · Mặt bằng (hình chiếu bằng)

Tờ 1/1 · Bản dự thảo